Snitt B
Snitt B
1.15
VF
A: 5,1 m²
GA-02
1.06
bitapp
A: 10,6 m²
1.04
EL
A: 1,3 m²
1.16
wc
A: 2,1 m²
1.17
wc
A: 2,1 m²
1.18
hc wc
A: 5,3 m²
1.05
Teknisk sjakt
A: 3,9 m²
1.20
energisentral
A: 47,8 m²
1.02
EL
A: 1,3 m²
1.03
Teknisk sjakt
A: 3,9 m²
energimåler?
1.09
gang
A: 42,6 m²
1.08
entre/vrimle
A: 49,5 m²
1.21
spiserom/utstilling
A: 144,1 m²
anretningskjøkken
Kjølesk.
Kjølesk.
Oppv.
Oppv.
YTTERVEGG BITRAPP MED LIGGENDE STENDERVERK
ZEB YV-223_Trepanel
ZEB YV-223+73_Trepanel/G
ZEB IV-98 G/G_R'w 35dB
ZEB IV-98 Q/G_R'w 35dB
ZEB IV-98 GG/GG_R'w 44dB_EI60
ZEB IV-98 F/F_EI60
ZEB IV-98_34dB_påforing
ZEB IV-98 GG/_sjakt
ZEB IV-198 GG/G_sjakt
ZEB IV-73_påforing sjakt
ZEB IV-G_34dB_påforing
ZEB IV-120 M
ZEB IV-68-30 G/_R'w 44dB_påforing
ZEB IV-75 FF/_EI60_sjakt
IV-02
Mål: 4 460x2 350
Bh= 900
EI 60
R'w 44 dB
VT-D-01
Rømningsdør
A-D-23-1-6-15
A-D-24-1-6-01
A-D-24-1-6-02
A-D-24-1-6-04
A-D-23-1-6-08
A-D-23-1-6-11
A-D-23-1-6-21
1
2
3
4
5
24 120
16 546
4 800
4 073
1 800
1 800
10 593
4 622
5 975
4 565
2 355
Rw>= 33 dB
Rw>= 43 dB
EI60S
Bh.=0
1 435
3 000
2 310
3 030
995
3 000
1 410 x 2 980
970 x 2 980
1 450 x 2 480
1 470
2 500

Snitt B
Snitt B
2.09
gang
A: 31,0 m²
2.08
gang
A: 19,8 m²
2.04
EL
A: 1,3 m²
2.14
bk
A: 1,3 m²
2.06
bitapp
A: 10,6 m²
2.15
hc wc
A: 4,1 m²
2.16
hc wc
A: 4,0 m²
2.05
teknisk sjakt
A: 3,9 m²
2.17
møte
A: 20,9 m²
2.18
teknisk styringsrom forskning
A: 27,2 m²
2.02
EL
A: 1,3 m²
2.03
teknisk sjakt
A: 3,9 m²
2.21
teknisk: tvillingrom
A: 7,7 m²
2.20
tvillingrom 2 forskning
A: 66,8 m²
Alle tilsluttende vegger mot tvillingrom skal utføres med samme tetthet som brannvegg
2.19
tvillingrom 1 forskning
A: 66,7 m²
Alle tilsluttende vegger mot tvillingrom skal utføres med samme tetthet som brannvegg
YTTERVEGG BITRAPP MED LIGGENDE STENDERVERK
ZEB YV-223+73_Solceller/G
GLASSPORT M. ADGANGSKONTROLL
ZEB IV-98 G/G
ZEB IV-98_34dB_påforing
ZEB IV-98 GG/_sjakt
ZEB IV-73_påforing sjakt
ZEB IV-G_34dB_påforing
ZEB IV-98 GG/GG_R'w 44dB
ZEB IV-98 G/G_R'w 35dB
ZEB IV-68-30 G/_R'w 44dB_påforing
ZEB IV-160 M_R'w 44dB
ZEB IV-98 GG/GG_R'w 37dB
ZEB IV-98 GG/GG_R'w 37dB_EI60
ZEB IV-98 GG/GG_R'w=44dB_påforing
ZEB IV-120 M
ZEB IV-98 GG/GG_R'w 44dB
A-D-24-2-6-02
A-D-24-2-6-04
A-D-24-2-6-06
A-D-24-2-6-08
A-D-24-2-6-10
A-D-24-2-6-12
A-D-24-2-6-14
A-D-24-2-6-16
A-D-24-2-6-05
A-D-23-2-6-10
A-D-23-2-6-05
A-D-23-2-6-16
A-D-23-2-6-14
A-D-23-2-6-12
A-PA-24-2-6-17
10x21M DI-K-10 EI30CS Rw>= 33 dB 2.06
10x21M SV-07 dør Rw>= 33 dB 2.17
17x25M DI-T-06 Rw>= 33 dB 2.20
17x25M DI-T-07 Rw>= 38 dB 2.19
10x21M DI-K-12 Rw>= 38 dB 2.21
10x21M DI-K-08 Rw>= 33 dB 2.15
10x21M DI-K-08 Rw>= 33 dB 2.16
23x25M SV-05 R'w 34 dB 2.12
R'w 34 dB SV-07 44x25M 2.17
Rw>= 33dB DI-T-02 10x25M 2.18
DI-K-02 8x21M 2.04
DI-K-01 8x21M 3.13
DI-K-02 8x21M 2.02
900 x 1 775 V-05
900 x 1 775 V-06
900 x 1 775 V-07
900 x 1 775 V-08
Bh.= 850
Bh.= 0
1 190 x 2 690 V-47
1 190 x 2 690 V-46
Ned
11 751
11 751
24 073
16 546
4 800
1 800
1 800
4 073
12 407
5 890
4 563
4 400
2 510
5 000
4 573
5 920
2 431
2 163
1 157
1 169
1 140
2 351
2 351
1 710
2 510
1 348
2 550
925
1 795
50
223
47
98
73
49
1
2
3
4
5
A
B
C
D
E
F
G
H

Snitt B
Snitt B
3.09
gang
A: 51,9 m²
3.08
gang
A: 32,2 m²
Absorbent
3.06
bitapp
A: 10,6 m²
10x21M
DI-K-10
EI30CS
Rw>= 33 dB
3.06
ZEB IV-98_34dB_påforing
3.04
EL
A: 1,3 m²
3.13
bk
A: 1,3 m²
3.12
Rw>= 33 dB
SV-03 dør
10x21M
16x25M
SV-03
R'w 34 dB
3.12
DI-K-02
8x21M
DI-K-01
8x21M
ZEB IV-98 G/G
ZEB IV-98 GG/_sjakt
3.05
Teknisk sjakt
A: 3,9 m²
ZEB IV-73_påforing sjakt
ZEB IV-120 M_EI60
3.14
hc wc
A: 4,1 m²
3.15
hc wc
A: 4,0 m²
10x21M
DI-K-08
Rw>= 33 dB
3.14
3.15
ZEB IV-98 G/G_R'w 35dB
ZEB IV-98 GG/G_R'w 35dB
ZEB IV-98 GG/GG_R'w 37dB
YTTERVEGG BITRAPP MED LIGGENDE STENDERVERK
ZEB YV-223+120 M_solcelle
1 190 x 2 690
V-47
Bh.=0
3.16
prosjektplass
A: 22,4 m²
3.17
R'w 34 dB
SV-06
37x25M
Rw>= 38 dB
SV-06 dør
10x21M
3.17-01
R'w 48 dB
SV-09
2 770 x 2 490
Bh.= 0
3.17
multirom
A: 11,2 m²
ZEB IV-98 GG/GG_R'w 44dB
3.18
R'w 34 dB
SV-01
15x25M
10x21M
SV-01 dør
Rw>= 38 dB
3.18
multirom
A: 10,8 m²
3.18-01
R'w 44 dB
SV-08
900 x 2 490
GLASSPORT M ADGANGSKONTROLL
3.19
Sjakt: tvillingrom
A: 4,5 m²
3.02
EL
A: 1,3 m²
ZEB IV-98 G/GG
3.03
Teknisk sjakt
A: 3,9 m²
ZEB IV-120 M
3.20
R'w 44 dB
SV-10
4 250 x 2 490
Ned
3.23
Rw>= 33 dB
SV-02 dør
10x21M
16x25M
SV-02
R'w 37dB
3.23
3.20
R'w 34 dB
SV-04
16x25M
10x21M
SV-04 dør
Rw>= 33 dB
3.23
adskilt arbeidsplass
A: 20,6 m²
3.22
åpen arbeidssone
A: 47,9 m²
3.21
åpne arbeidsplasser
A: 18,9 m²
3.20
møte
A: 27,3 m²
ZEB IV-98 G/G_R'w 35dB
ZEB IV-98 GG/GG_R'w 37dB
ZEB YV-223+73_Solceller/G
1 150 x 1 890
V-14
V-10
V-12
V-16
2 330 x 1 890
V-30
V-31
V-32
V-15
V-11
1 190 x 2 690
V-46
Bh.= 800
A-D-23-3-6-08
A-D-23-3-6-03
A-D-23-3-6-01
A-D-24-3-6-03
A-D-23-3-6-10
24 073
11 902
16 546
16 127
7 198
7 226
4 800
4 073
1 800
5 750
4 751
4 702
4 750
2 351
1 205
1 279
1 492
2 350
1 910
1 170
50
223
47
A
B
C
D
E
F
G
H
1
2
3
4
5

Snitt B
Snitt B
4.06
bitapp
A: 11,0 m²
4.07
ventilasjonsrom
A: 82,1 m²
4.03
gang
A: 29,6 m²
4.08
inverterrom
A: 39,3 m²
4.10
Lager
A: 12,5 m²
4.09
hovedtavlerom
A: 16,5 m²
2 m
1,5 m = grense målbart areal
YTTERVEGG BITRAPP MED LIGGENDE STENDERVERK
ZEB YV-223+73_Solceller/G
ZEB IV-98_34dB_påforing
ZEB IV-148 GG/GG_R'w 37dB_losholt h 4m
ZEB IV-148 GG/GG_R'w 44dB_losholt h 4m
ZEB IV-68-30 G/_R'w 44dB_påforing
ZEB IV-120 M
ZEB IV-G_34dB_påforing
ZEB IV-98 F/F_EI60
ZEB IV-98 GG/GG_R'w 44dB
ZEB IV-98 F/F_EI60_R'w 37dB
ZEB IV-98 G/G
ZEB YV-223+73_Solceller/G
10x21M
DI-K-10
EI30CS
Rw>= 33 dB
4.06
4.07-2
Rw>= 38 dB
DI-T-05
20x27M
4.05
Rw>= 38 dB
DI-T-04
15x27M
IV-03
Mål: 4 400x2 710
Bh= 0
4.07
R'w 44dB
10x20M
DI-T-01
Rw>= 38 dB
4.07-1
10x21M
DI-K-11
EI60S
Rw>= 38 dB
4.08
4.10
DI-K-22
10x21M
4.09
Rw>= 38 dB
EI60S
DI-K-13
10x21M
A-D-24-4-6-03
1 190 x 2 690
V-47
1 190 x 2 690
V-46
Bh= 0
1 800
4 800
1 800
4 073
16 546
4 677
4 677
4 517
4 538
2 010
2 710
4 400
2 710
1 010
2 110
1 140
1 042
2 350
9 502
3 675
2 051
A
B
C
D
E
F
G
H
1
2
3
4

nitt B
Snitt B
4.07-2
Rw>= 38 dB
DI-T-05
20x27M
4.05
Rw>= 38 dB
DI-T-04
15x27M
IV-03
Mål: 4 400x2 710
Bh= 0
4.07
R'w 44dB
ZEB IV-98_34dB_påforing
ZEB IV-148 GG/GG_R'w 37dB_losholt h 4m
ZEB IV-148 GG/GG_R'w 37dB_losholt h 4m
ZEB IV-148 GG/GG_R'w 44dB_losholt h 4m
ZEB IV-148 GG/GG_R'w 44dB_losholt h 4m
Bh.= 3 690
1 180 x 980
Lufteluke
4.06
YTTERVEGG BITRAPP MED LIGGENDE STENDERVERK
R'w 44dB_påforing
R'w 44dB_påforing
4.07
ventilasjonsrom
4.03
gang
ZEB IV-98 F/F_EI60
ZEB IV-98 F/F_EI60
ZEB IV-98 GG/GG_R'w 44dB
ZEB YV-223+73_Solceller/G
ZEB YV-223+73_Solceller/G
ZEB YV-223
2 m
1,5 m = grense målbart areal
1 800
4 800
1 800
4 073
16 546
16 546
1
2
3
4
5
1
2
3
4
5
A
B
C
D
E
F
G
H

Snitt B
Snitt B
5
4
Takvinkel
30 grader
3
3
2
2
1:40
1:40
1:40
1:40
1:40
1:40
1
1
B
C
A
D
E
F
G
H

780
330
3 070
3 520
+51,430
+49,500
330
780
3 070
3 520
+47,580
+45,650
330
780
3 070
3 520
+43,730
+41,800
330
780
1 100
1 550
+39,920
330
870
V-34
V-21
V-21
V-21
V-24
V-21
V-23
V-21
V-22
V-21
V-38
V-34
V-21
V-23
V-25
V-23
V-25
V-23
V-21
V-24
V-21
VT-S-02
VT-S-08
VT-S-06
V-25
VT-S-10
V-23
V-25
V-23
V-25
V-23
V-23
V-24
VT-S-03
VT-S-09
V-39
VT-S-13
V-43
330
2 050
330
2 090
330
330
2 090
330
2 050
330

000
V-16
V-30
V-31
V-32
V-31
V-32
V-31
V-32
V-31
V-15
V-07
V-05
V-08
V-05
V-06
V-08
V-05
V-06
V-05
V-08
V-07
V-05
V-08
V-05
V-06
V-08
V-05
V-05
V-06
V-08
+39,92

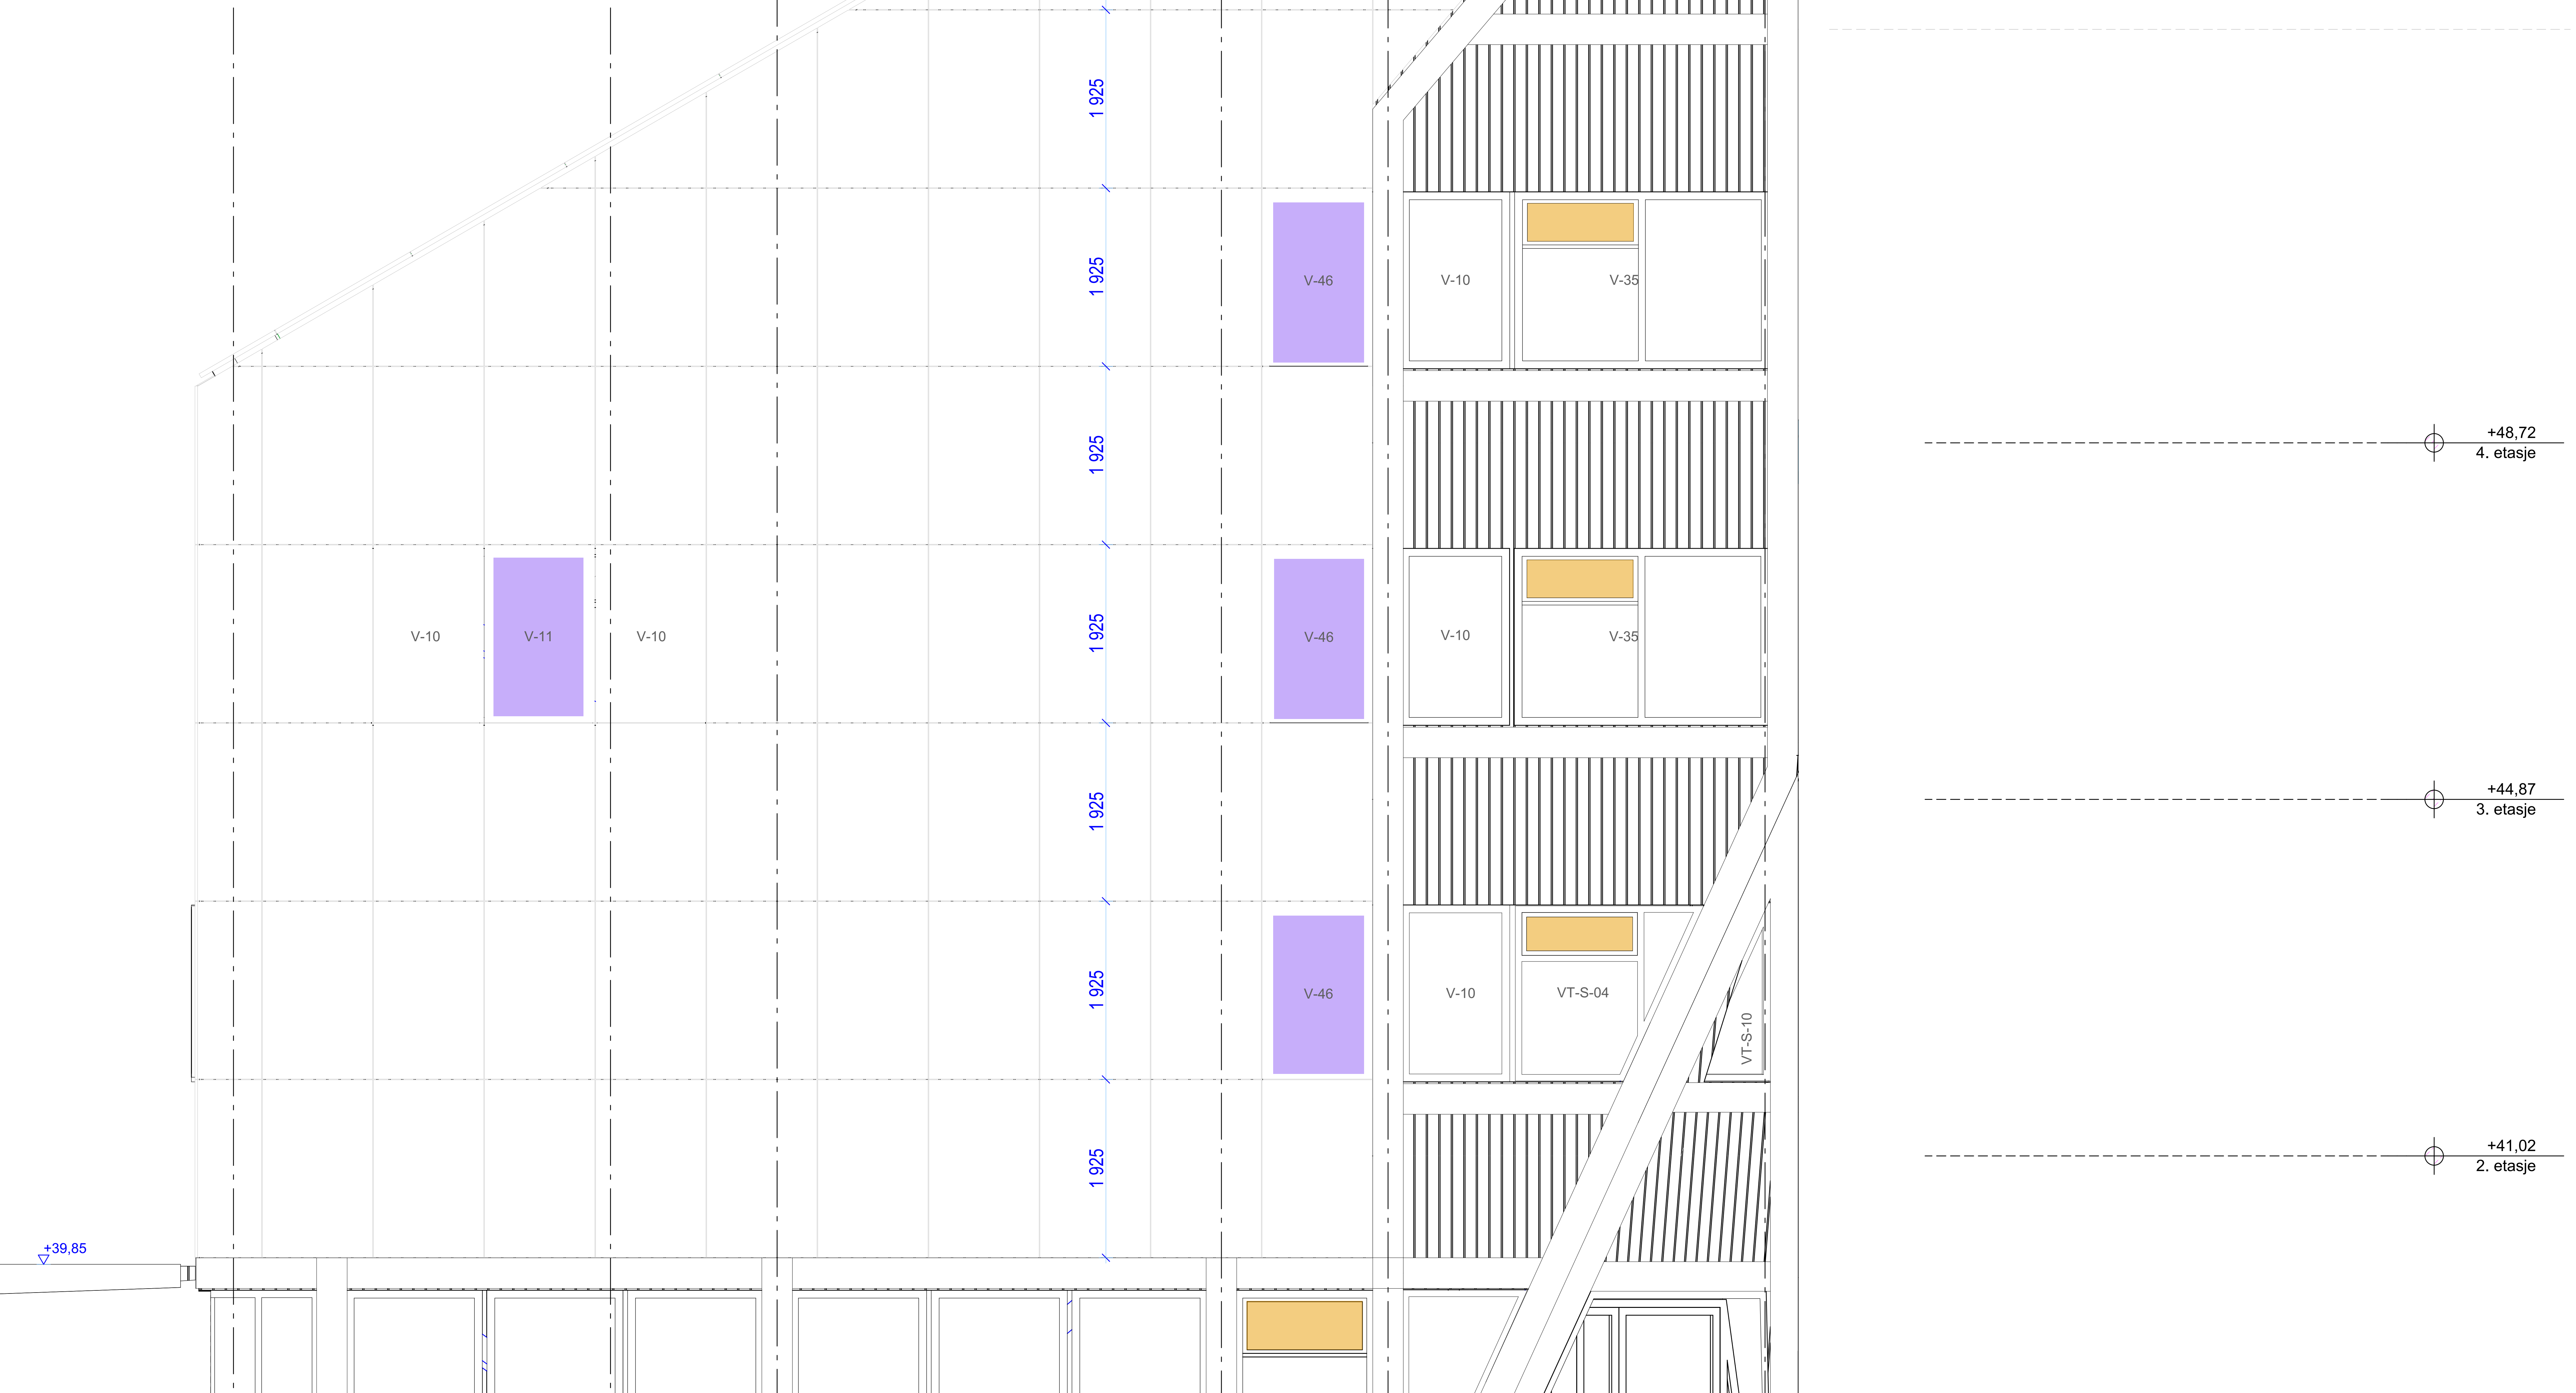

MMI 6.0

6.0	07.06.19	Ove
Rev.	Dato	Rev

Fasade
Fasade

ARBEI

Tiltakshaver
NTNU

Entreprenør
Veidek

Prosjektnummer
62714

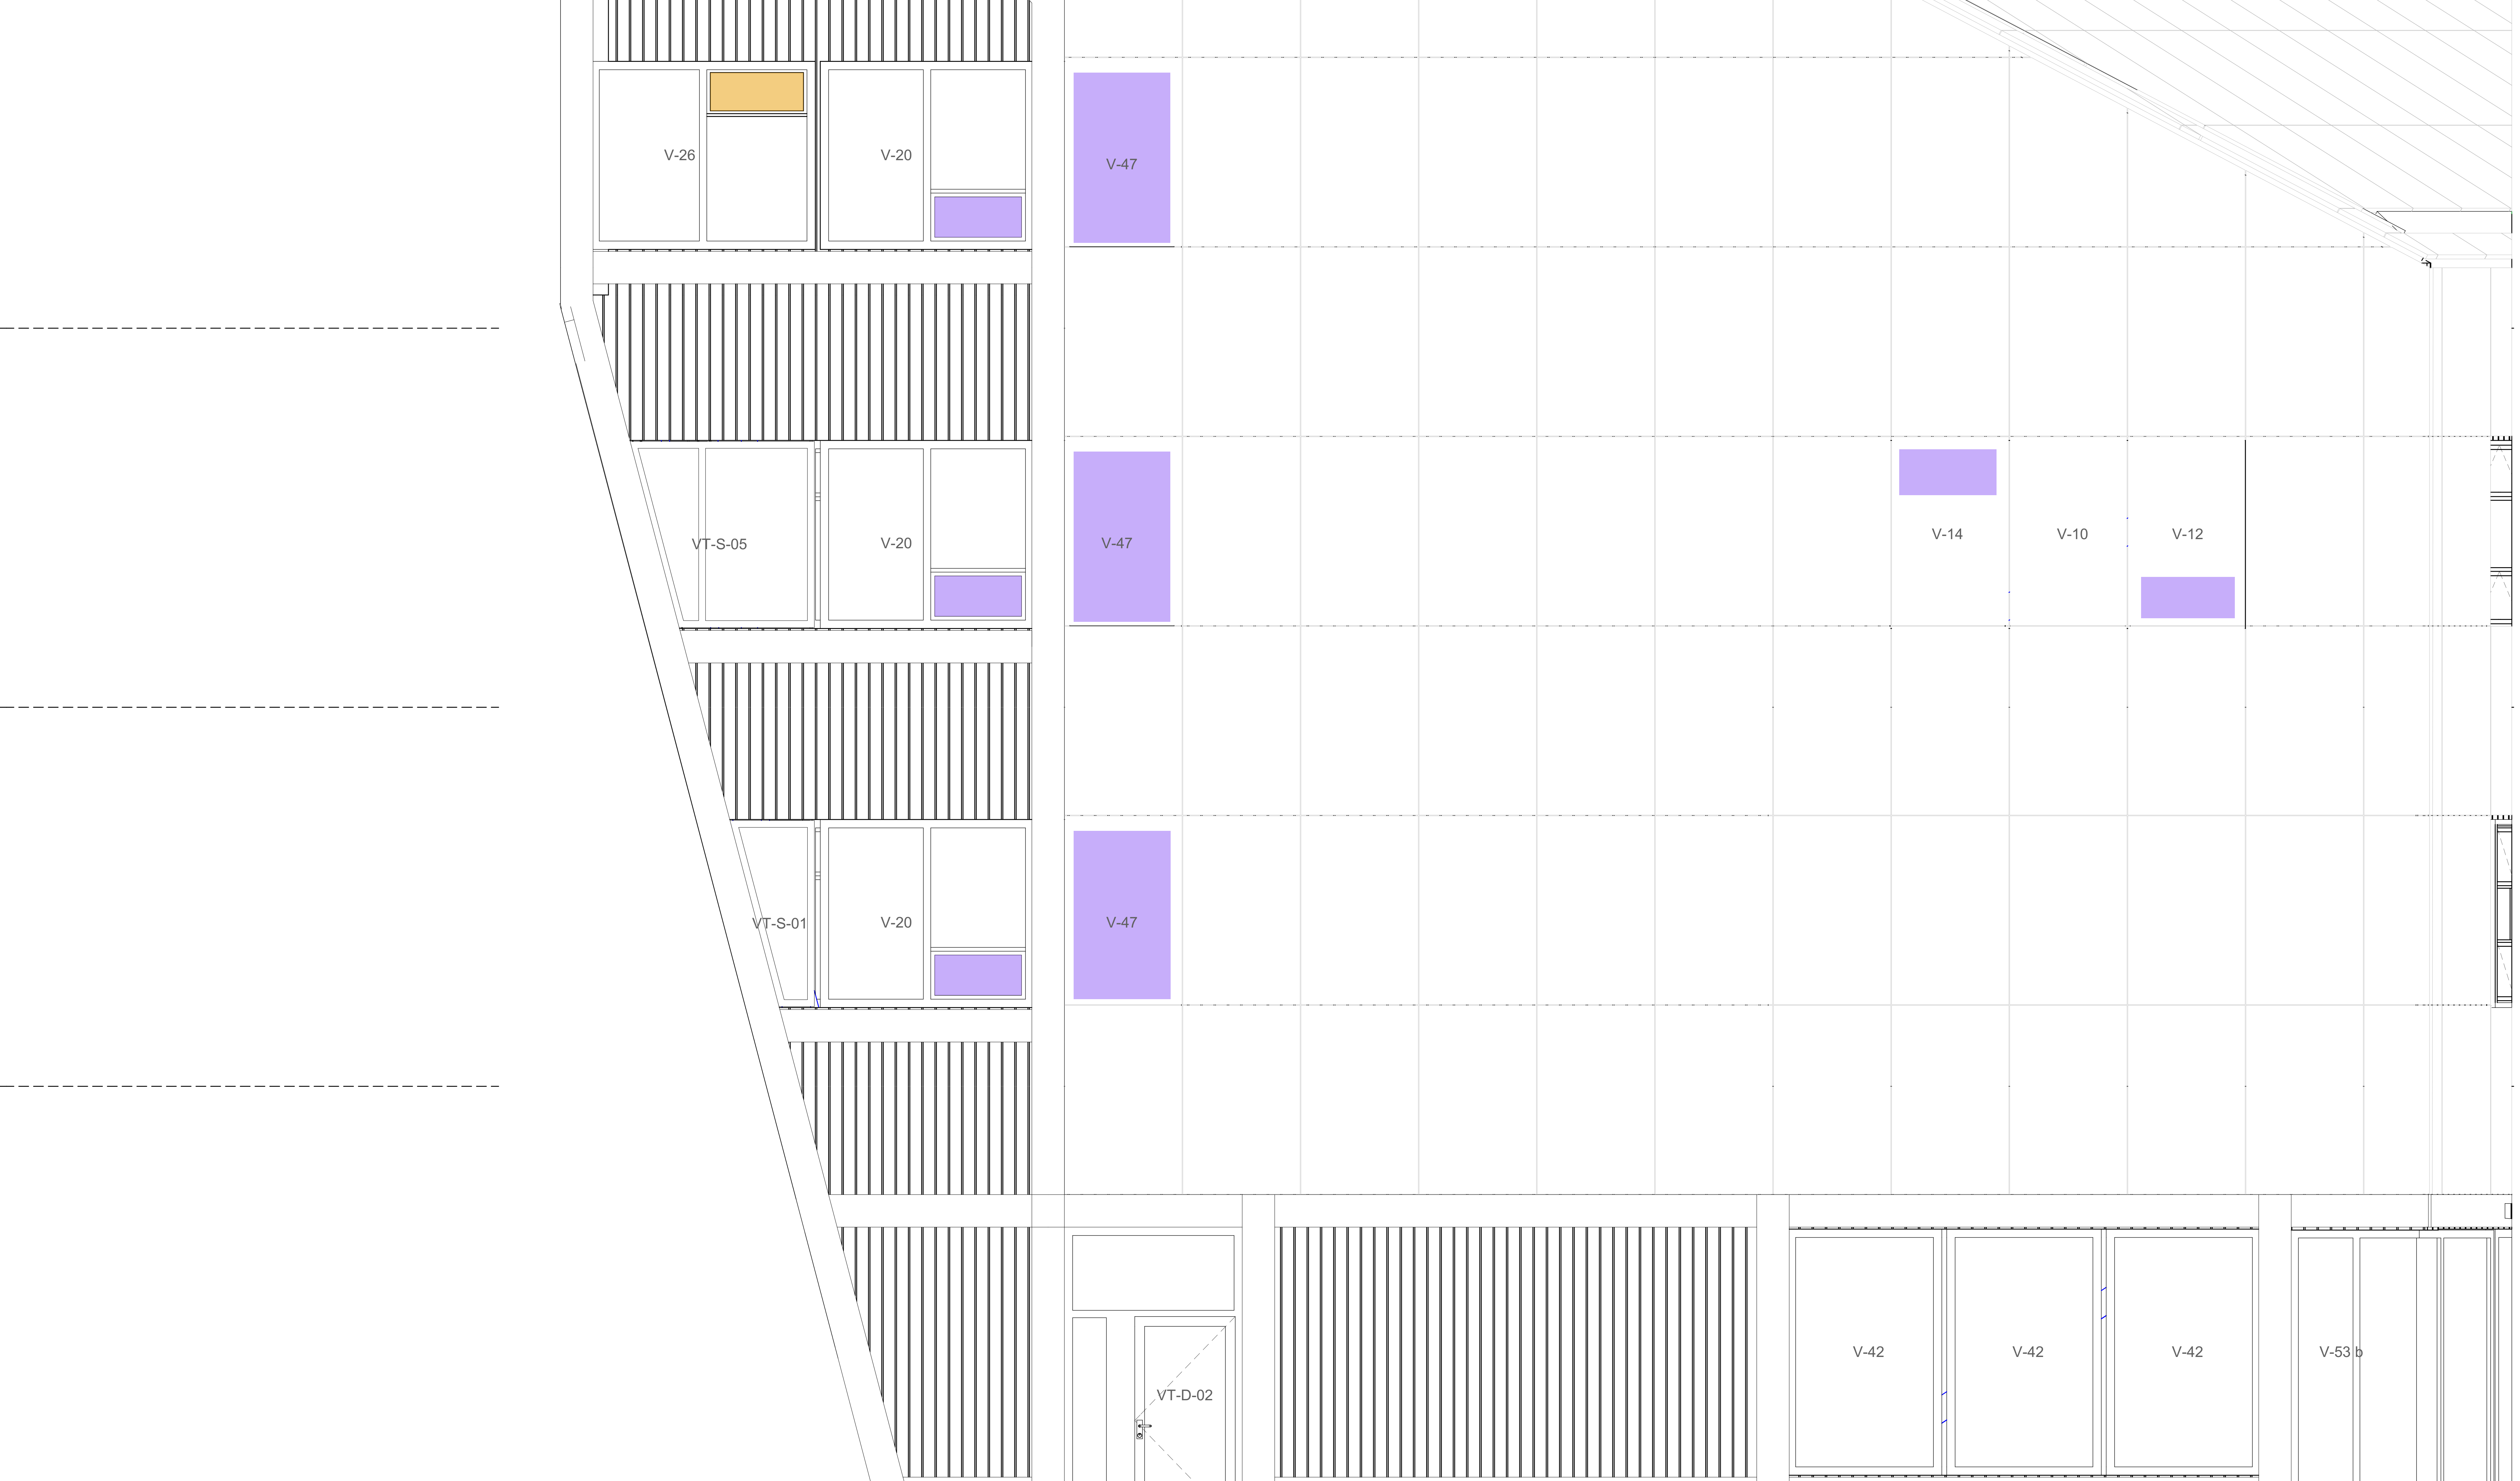

MMI 6.0

Rev.	Dato	Rev
6.0	07.06.19	Ove

Fasade
Fasade

ARBEI

Tiltakshaver
NTNU

Entreprenør
Veidek

Prosjektnummer
62714

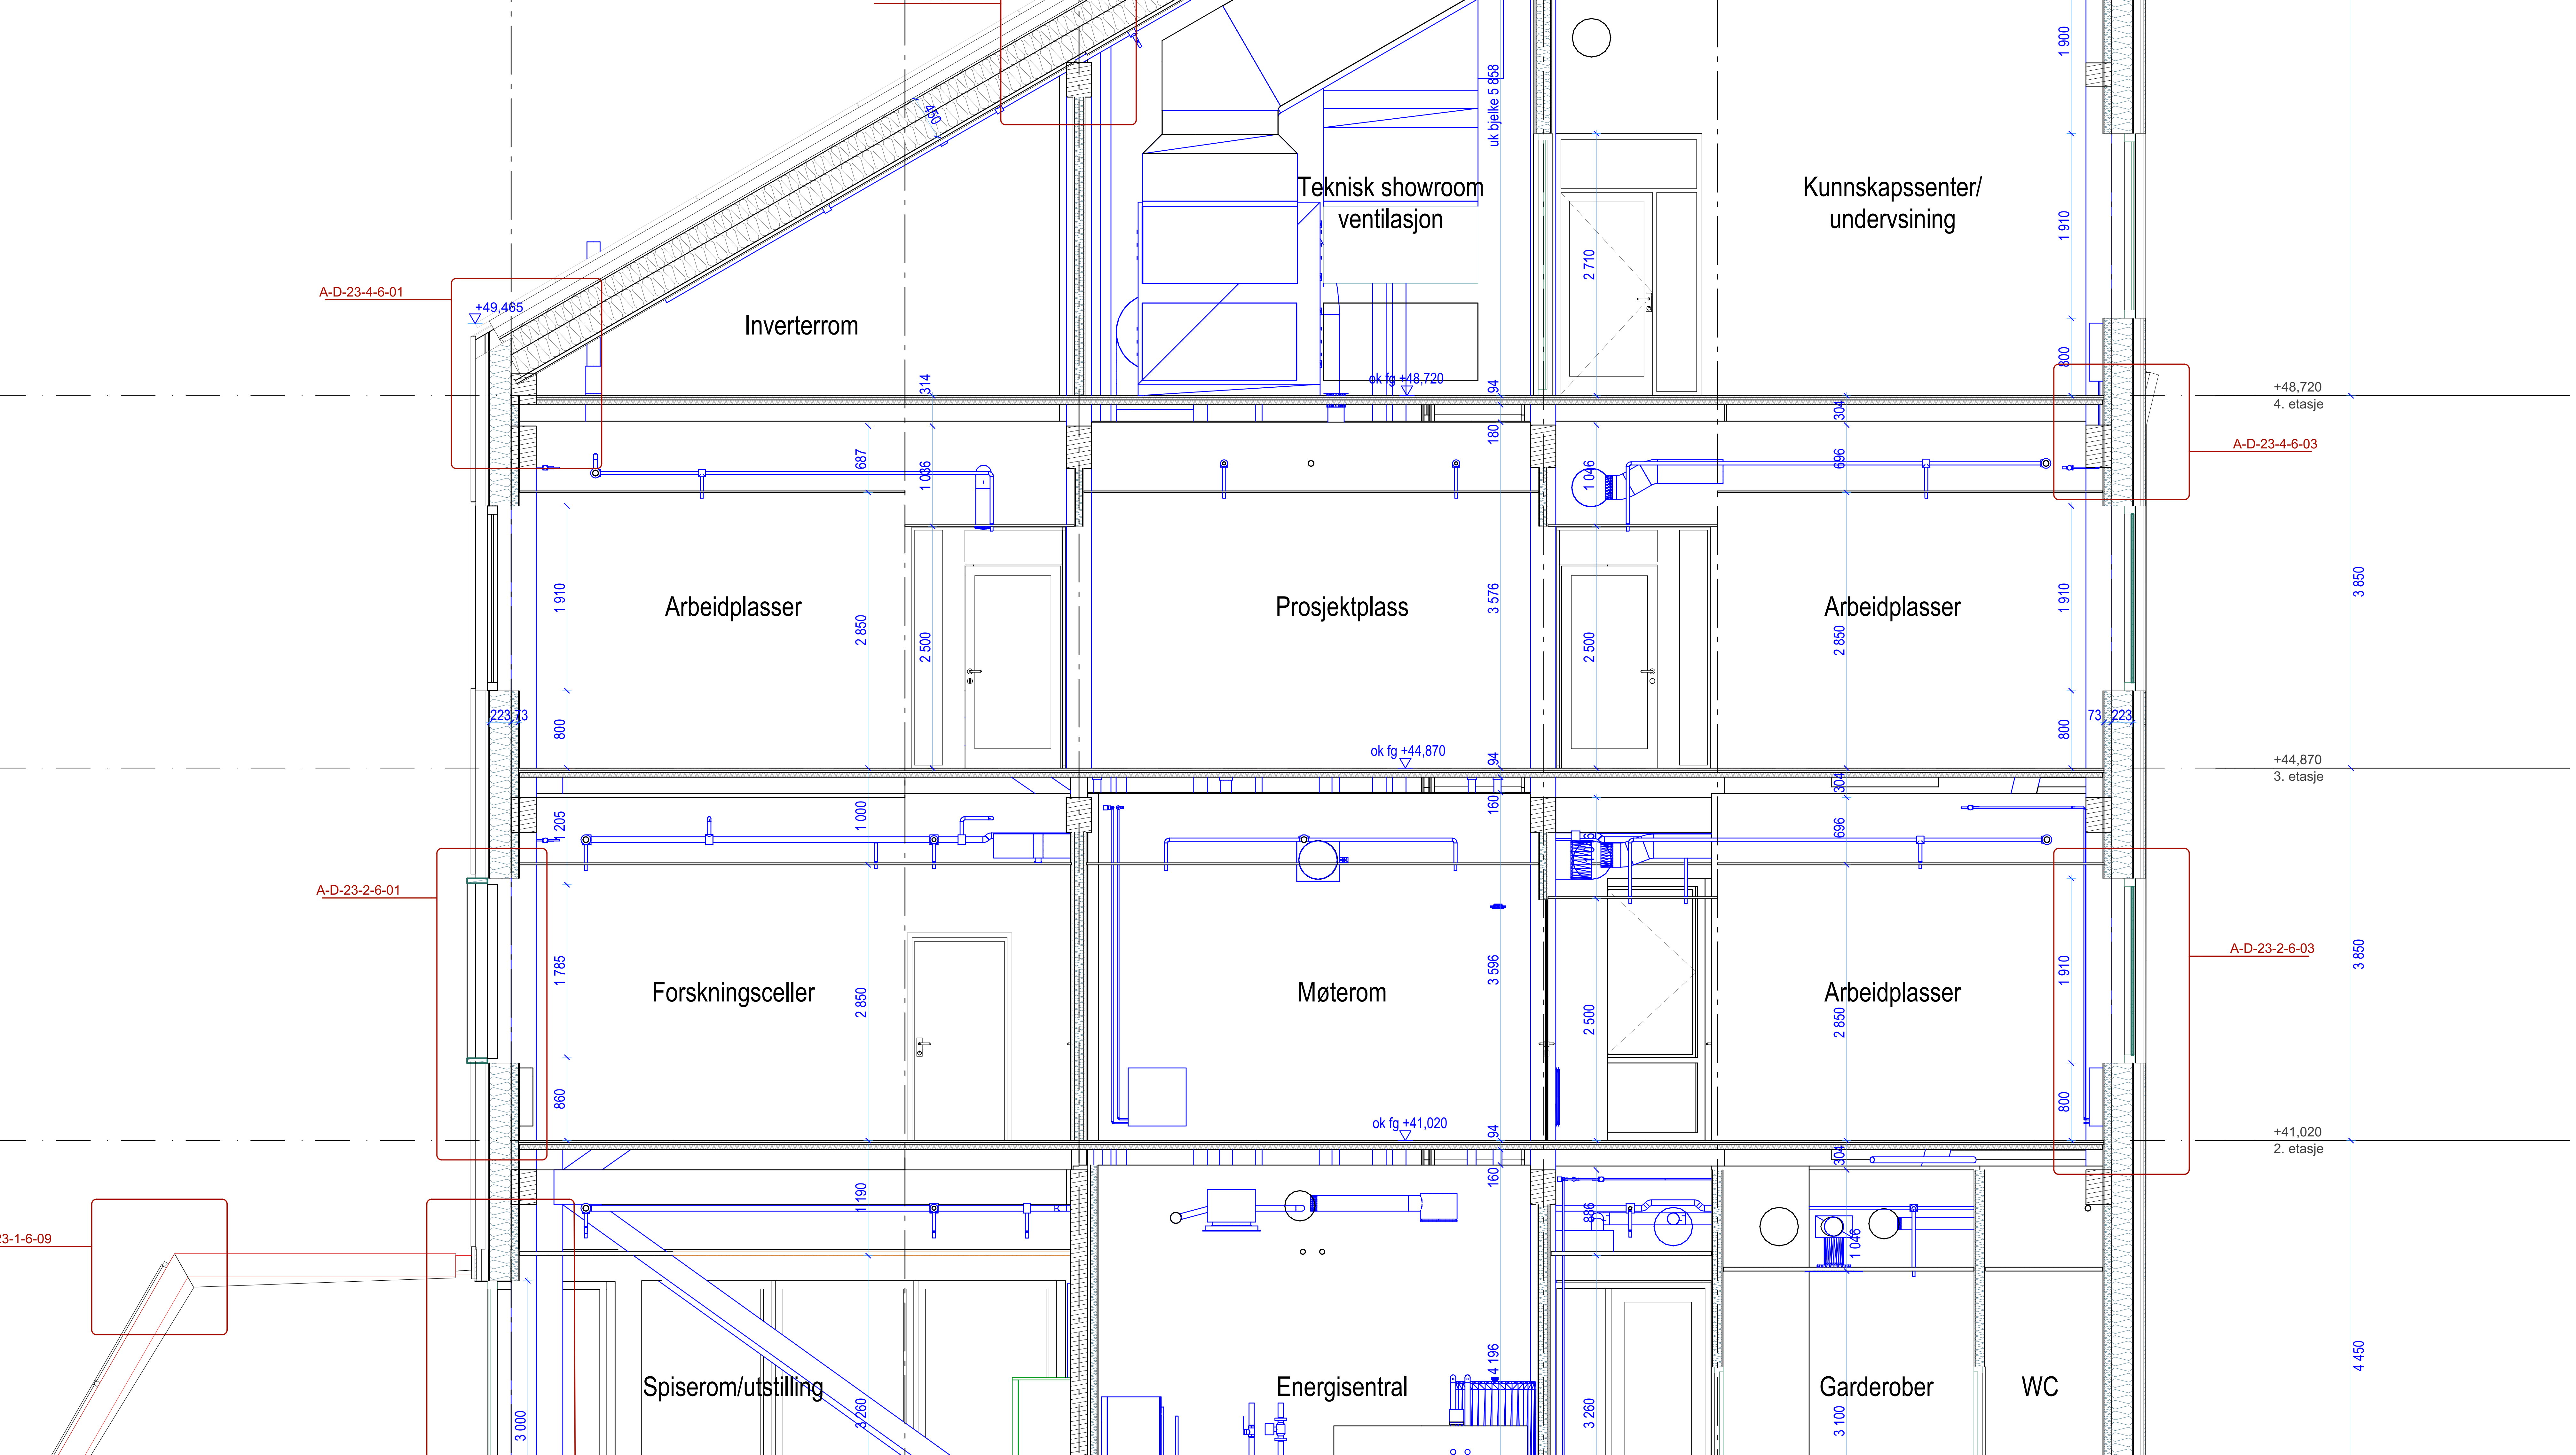

MMI 6.0

6.0	07.06.19	Ove
Rev.	Dato	Rev

Snitt 1
Tverrs

ARBEI

Tiltakshaver
NTNU

Entreprenør
Veidek

Prosjektnummer
62714

Bi-trapp
Teknisk showroom
ok fg +48,720
+48,720
4. etasje
3 690
1 350
1 000
Multirom
Multirom
Prosjektplass
Bøttekott
2 500
2 850
2 850
2 500
ok fg +44,870
+44,870
3. etasje
3 850
223
73
1 350
1 000
1 350
Sjakt
Teknisk styringsrom
Møte
Bøttekott
Sjakt
3 756
2 500
2 850
2 500
A-D-24-2-6-03
ok fg +41,020
+41,020
2. etasje
3 850
Hovedtrapp
1 190
1 190
350
2 500
3 260
4 356
MCP
MCP
Energisentral
3 260
3 100
WC
4 450

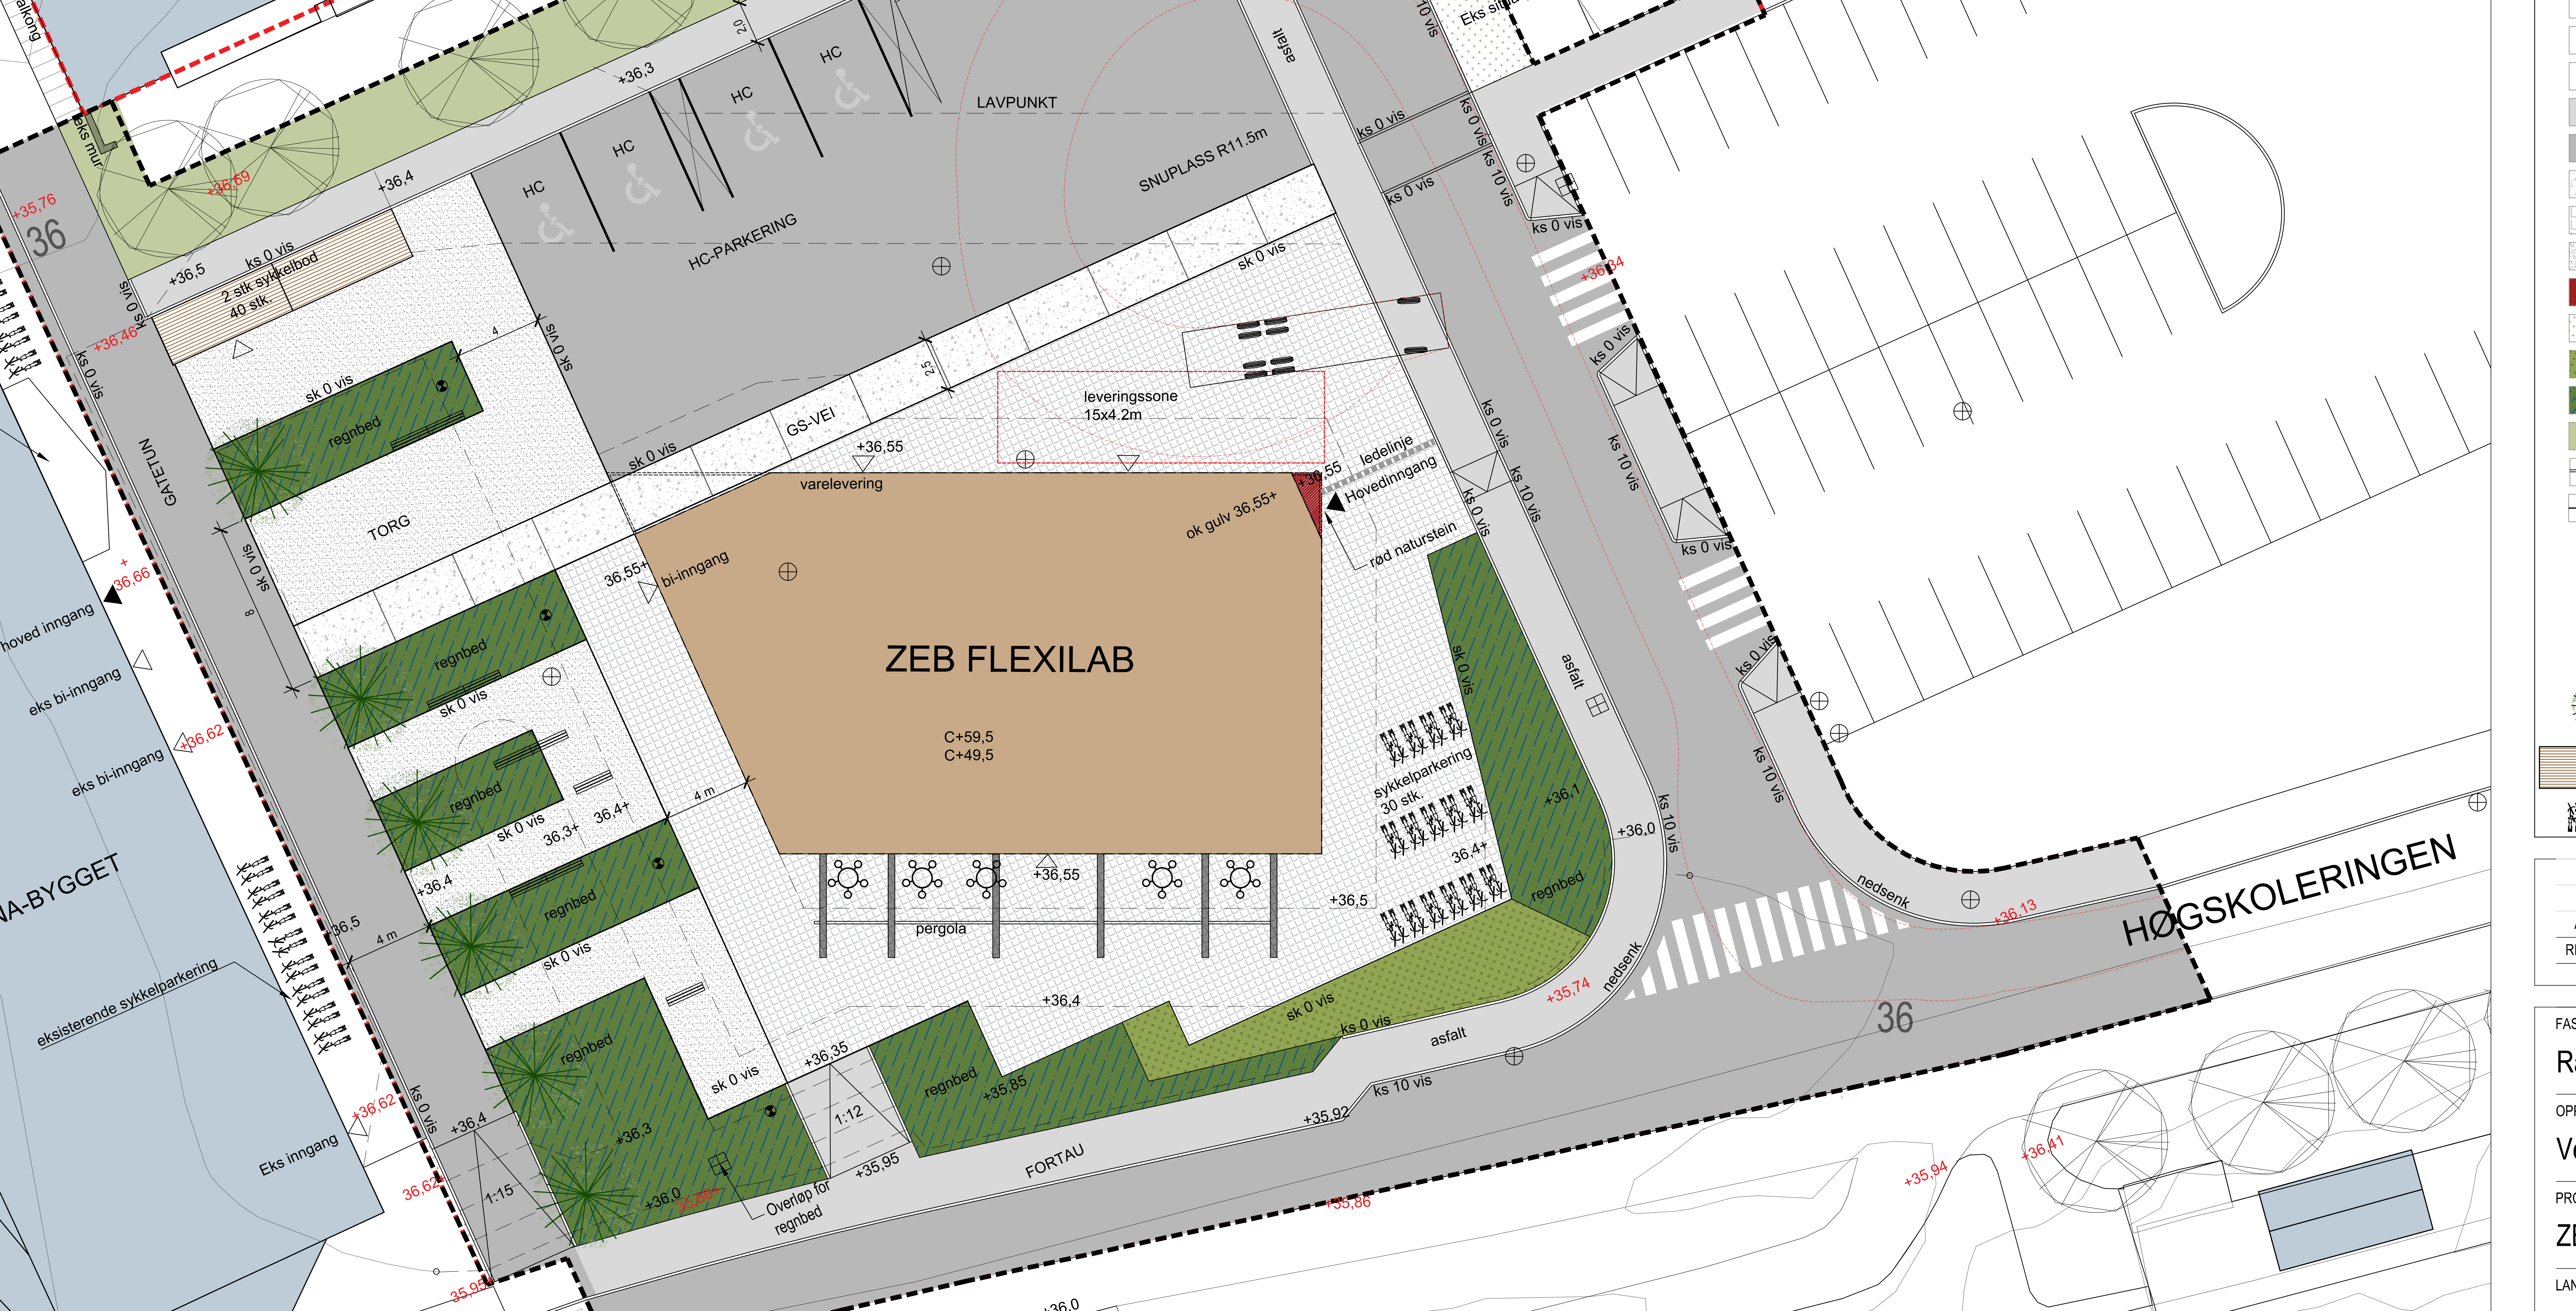
ZEB FLEXILAB
C+59,5
C+49,5
varelevering
ok gulv 36,55+
bi-inngang
36,55+
Hovedinngang
ledelinje
rød naturstein
leveringssone
15x4,2m
SNUPLASS R11,5m
LAVPUNKT
HC-PARKERING
HC
HC
HC
HC
GS-VEI
TORG
GATETUN
regnbed
regnbed
regnbed
regnbed
regnbed
regnbed
regnbed
sk 0 vis
ks 0 vis
ks 10 vis
2 stk sykkelbod
40 stk.
sykkelparkering
30 stk.
pergola
asfalt
FORTAU
nedsenk
Overløp for
regnbed
1:12
1:15
4 m
4 m
HØGSKOLERINGEN
NA-BYGGET
hoved inngang
eks bi-inngang
eks bi-inngang
eksisterende sykkelparkering
Eks inngang
36
36
+36,55
+36,5
+36,4
+36,35
+36,3
+36,3
+36,0
+36,1
+35,85
+35,95
+35,92
+35,74
+36,13
+36,41
+35,94
+35,86
+36,62
+36,62
+36,66
+36,46
+35,76
+36,69
+36,84
+36,0
+36,4+
36,4+
36,3+